
© 2026 Copyright Of This Drawing Is Held With S G Design Studio Ltd.
This Drawing Is Not To Be Scaled From By Contractors / Developers.
To Be Read In-Conjunction With All Architects And Engineers' Drawings.
All Dimensions, Spans And Roof Pitches Are To Be Checked Before Works Commence And Fabrication.
Discrepancies Are To Be Reported To S G Design Studio Limited Immediately.

PLEASE NOTE, THE CLIENT IS RESPONSIBLE TO PASS ONTO THE CONTRACTOR / MAIN CONTRACTOR (PRINCIPAL CONTRACTOR) IN WRITING, THEIR RESPONSIBILITIES UNDER THE CDM REGULATIONS 2015

IT IS THE MAIN CONTRACTORS RESPONSIBILITY (PRINCIPAL CONTRACTOR) TO CARRY OUT THEIR DUTIES UNDER THE CDM REGULATIONS 2015
THIS ACT CAME INTO FORCE ON THE 6TH APRIL 2015

THESE REGULATIONS APPLY TO ALL PROJECTS, BOTH RESIDENTIAL / COMMERCIAL EXTENSIONS, ALTERATIONS AND NEW BUILDS.

Note, Whilst S G Design Studio Ltd is the Principal Designer for this Project under (BSA) Building Safety Act 2023.
S G Design Studio Ltd is ONLY the principal designer up until the Building Regulations (Full Plans) Application has been submitted and approved / conditionally approved by the Local Authority Building Control / Approved Inspector.
As S G Design Studio Ltd does not carry out site inspections during the works, this role needs to be passed onto the Main Contractor or Client.

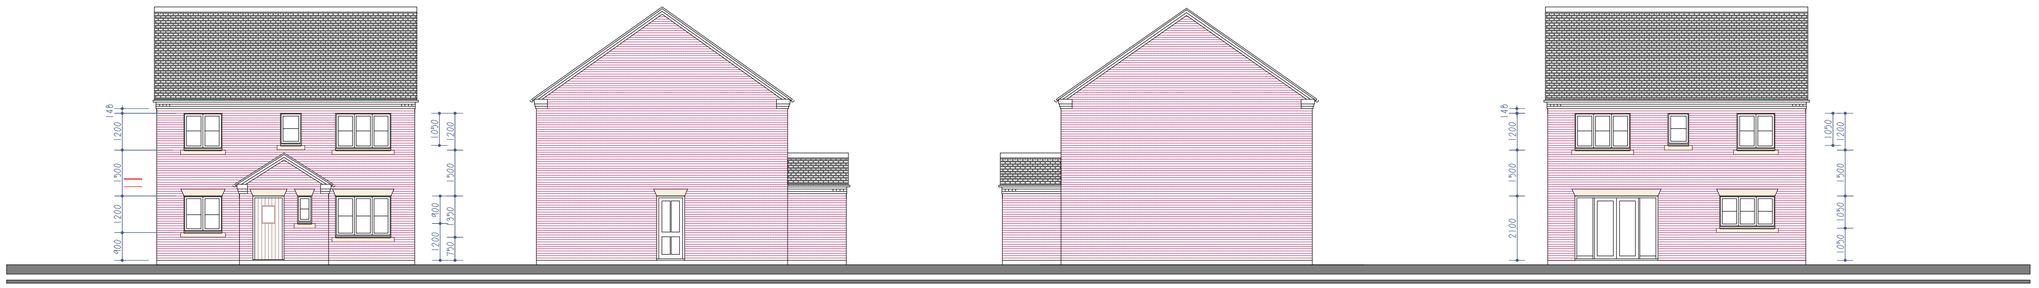


PROPOSED FRONT


PROPOSED SIDE

PROPOSED SIDE


PROPOSED REAR

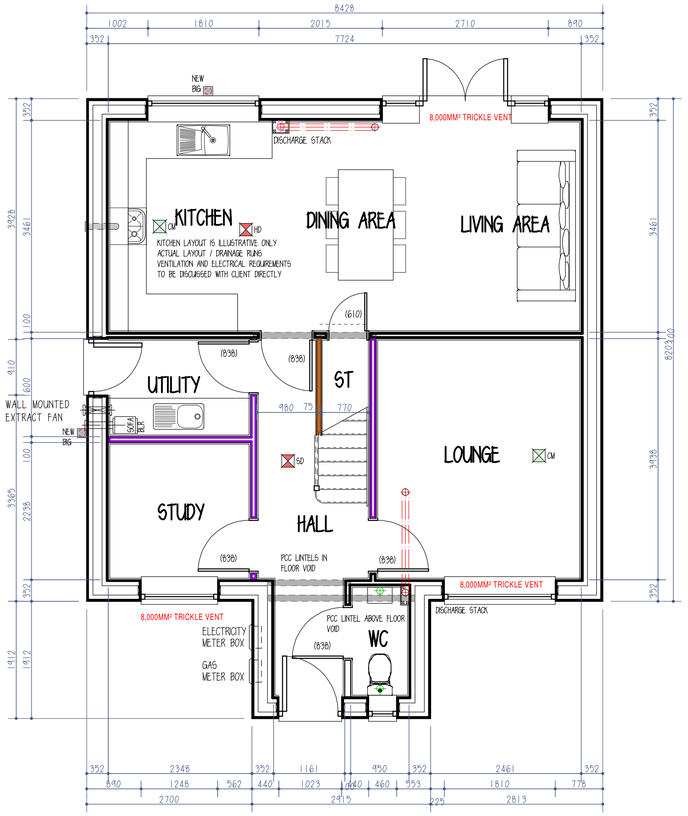

PROPOSED GROUND FLOOR PLAN

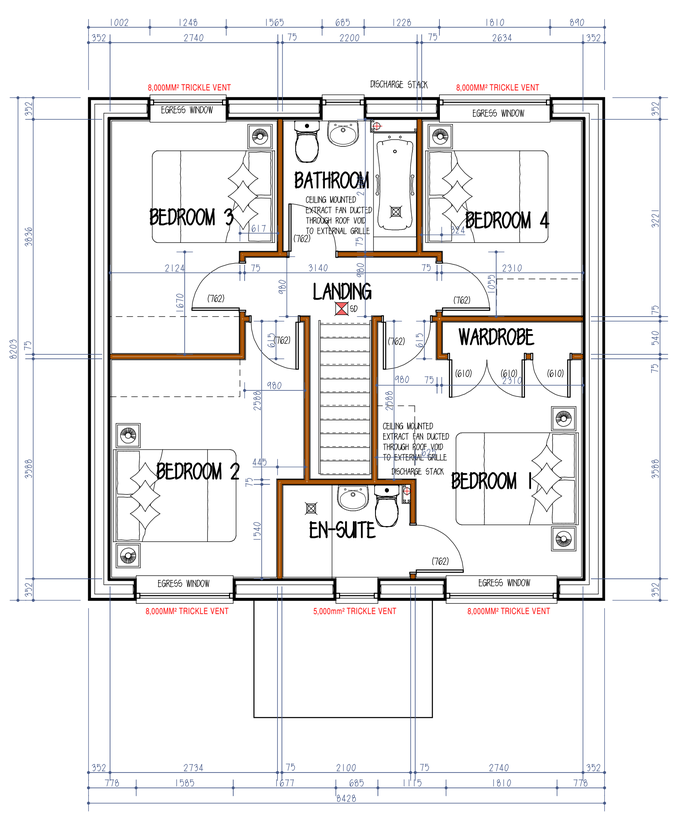

PROPOSED FIRST FLOOR PLAN

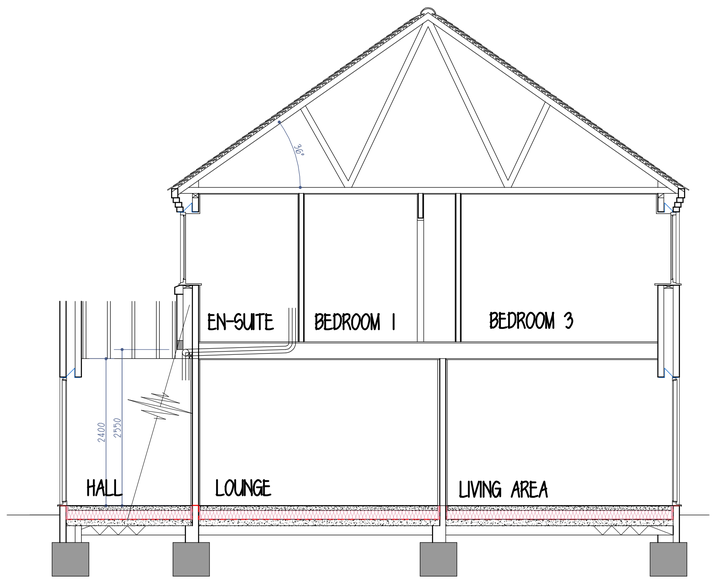

SECTION

KEY

- AS EXISTING / AS SURVEYED
- EXISTING TO BE REMOVED
- NEW STRUCTURAL CAVITY WALL
- NEW STRUCTURAL BLOCKWORK WALL
- NEW NON STRUCTURAL BRICKWORK / BLOCKWORK WALL
- NEW STRUCTURAL STUD PARTITION
- NON STRUCTURAL PARTITION (STUD)
- NEW INSULATED PARTITION (STUD)
- NEW STEEL STRUCTURAL BEAM OVER
- NEW TIMBER STRUCTURAL BEAM OVER
- NEW PCC LINTEL OVER
- EXISTING STRUCTURAL STEEL BEAM OVER
- EXISTING TIMBER STRUCTURAL BEAM / TRUSS OVER
- DENOTES STRUCTURAL PADSTONE
- (838) OR (762) — FIGURE DENOTES DOOR WIDTH PLUS FRAME
- SD / HD — SMOKE / HEAT DETECTOR - INTER CONNECTED
- CM — CARBON MONOXIDE DETECTOR
- EXTRACTOR FAN
- 8,000mm² OR 5,000mm² — REQUIRED TRICKLE VENTILATION
- RWP — RAINWATER PIPE
- DISCHARGE STACK — SOIL & VENT PIPE / DISCHARGE STACK
- 450 — BELOW SLAB DRAINAGE CONNECTIONS
- NEW / EXISTING — FOUL WATER DRAIN
- STORM WATER DRAIN
- NEW FOUNDATION SHOWN DASHED

DISTANCE IN METRES AT 1:1250 SCALE
0 10 20 30 40 50 60 70 80 90 100 110 120 130 140 150 160 170 180 190 200 210 220 230 240
0 20 40 60 80 100 120 140 160 180 200 220 240 260 280 300 320 340 360 380 400 420 440 460 480
DISTANCE IN METRES AT 1:2500 SCALE
SCALE BAR TO BE USED TO CHECK DRAWING PLOT ACCURACY ONLY

DISTANCE IN METRES AT 1:200 SCALE
0 2 4 6 8 10 12 14 16 18 20 22 24 26 28 30 32 34 36 38 40
0 10 20 30 40 50 60 70 80 90 100
DISTANCE IN METRES AT 1:500 SCALE
SCALE BAR TO BE USED TO CHECK DRAWING PLOT ACCURACY ONLY

DISTANCE IN METRES AT 1:100 SCALE
0 1 2 3 4 5 6 7 8 9 10 11 12 13 14 15 16 17 18 19 20
0 1 2 3 4 5 6 7 8 9 10
DISTANCE IN METRES AT 1:50 SCALE
SCALE BAR TO BE USED TO CHECK DRAWING PLOT ACCURACY ONLY

rev

designstudio architectural services
202 woodville road hartshorne swadlincote derbyshire de11 7ex
tel - 01283 226771 e-mail - mail@sgdesignstudio.co.uk

drawing
Proposed Dwelling
Type E

project
Land Off Brunt Lane
Woodville
Swadlincote

SE11

client
Premier Property (Central) Ltd

date 04/08/2026 revision nil -/-/-

scale 1:50 1:100 1:500 & 1:1250 at a1 size

drawing sheet size - a1 sized - landscape

drawing number 226-35-TP-E-10 nil

printed 04/08/2026 name 226-35-TP-E-10 rev nil A1